Në mungesë të shënimeve grafike për parcelën 1084-29 (në të cilën gjindet objekti në trajtim për legalizim) janë matur kufinjët faktik të parcelës në fjalë në koordinatat e pikave që janë paraqitur në manual!

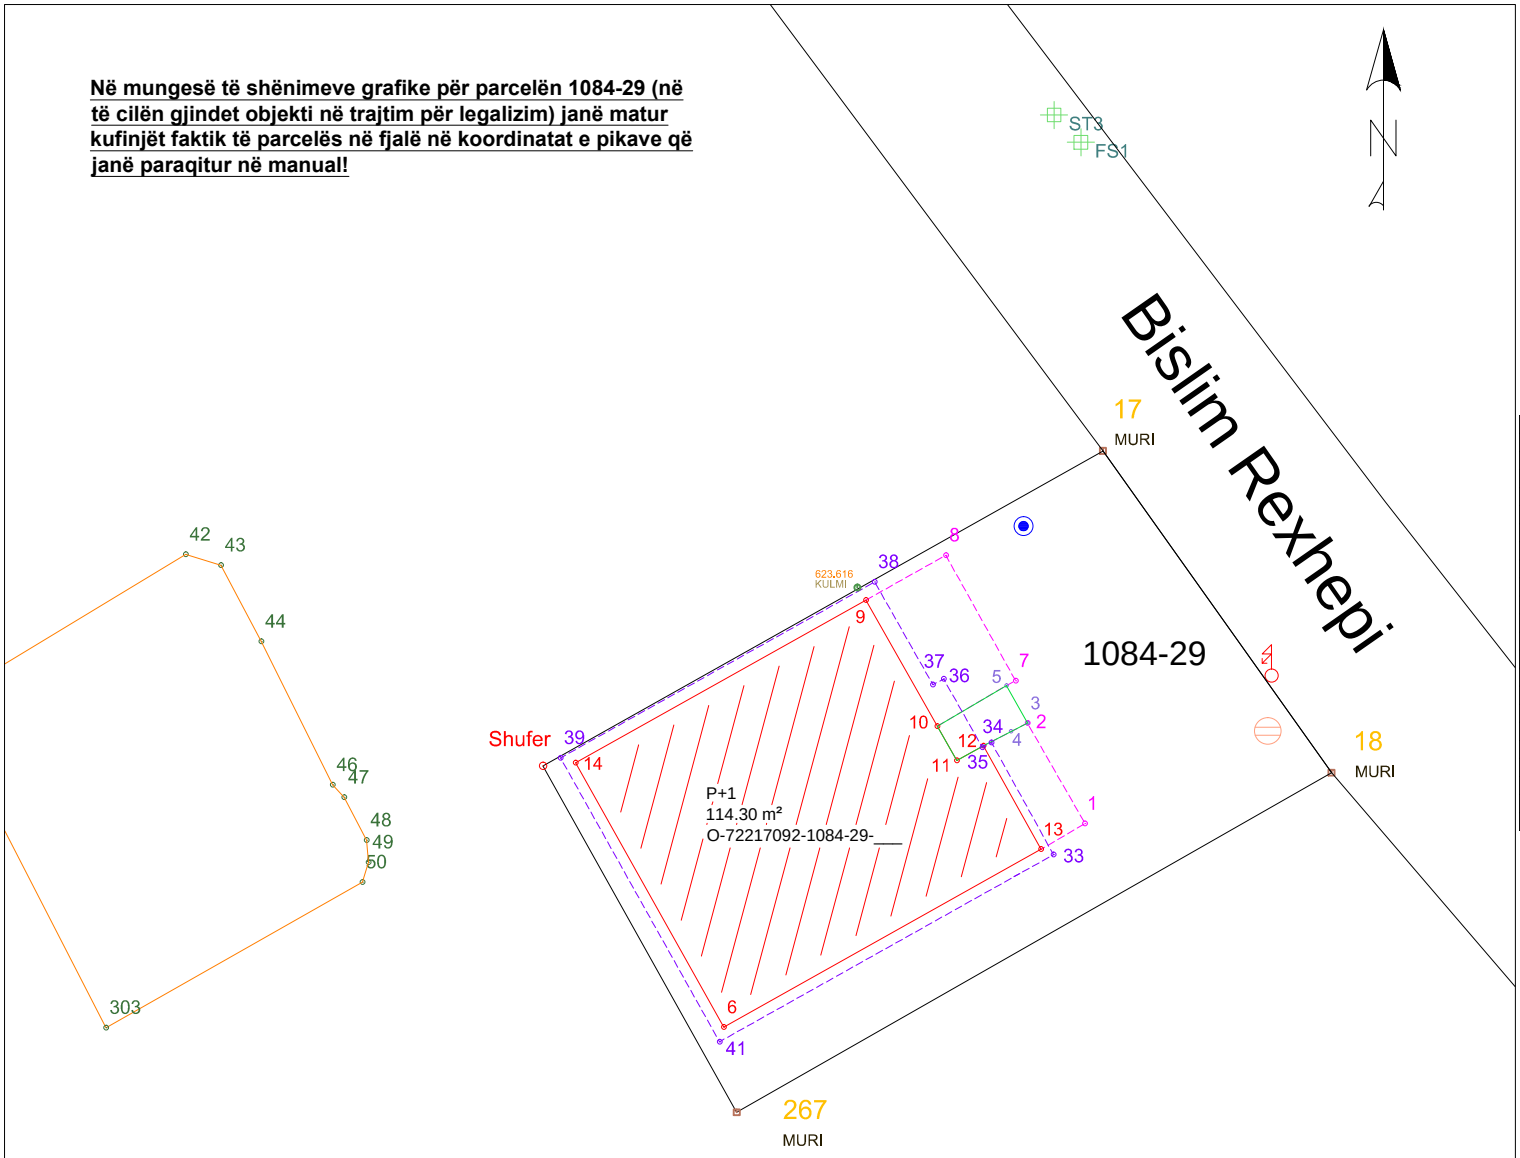

Nr	Y	X	H	Kodi	Përshkrimi	Burimi
9	7513227.608	4691401.480	616.454	40	Shtëpi-Ndërtesë	PM
10	7513229.972	4691397.314	616.454	40	Shtëpi-Ndërtesë	PM
11	7513230.620	4691396.176	616.454	40	Shtëpi-Ndërtesë	PM
12	7513231.491	4691396.664	616.454	40	Shtëpi-Ndërtesë	PM
13	7513233.403	4691393.245	616.454	40	Shtëpi-Ndërtesë	PM
14	7513218.014	4691396.106	616.454	40	Shtëpi-Ndërtesë	PM

Republika e Kosovës

Qeveria -Vlada

Ministria e Mjedisit dhe Planifikimit Hapësinr /Ministarstv Sredine i Prstrng Planiranja

AGJENCIA KADASTRALE E KOSOVËS/ KATASTARSKA AGENCIJA KOSOVA

Situacioni i terrenit

Zyra kadastrale kmunale / pštinska katastarska kancelarija: Ferizaj

Zona kadastrale / Katastarska zona: Ferizaj

Nr. i njësisë kadastrale / Br. katastarske jedinice : 1084-29

Numri i lëndës / Broj predmeta: _____

Shkalla e zvoglimit / Razmera plana 1: 250

Lista e koordinatave të pikave të matura:

Nr	Y	X	H	DSC
1	7513234.856	4691394.098	616.454	PERDHESA-TERAS
2	7513232.952	4691397.414	616.454	PERDHESA-TERAS
6	7513222.909	4691387.367	616.454	PERDHESA-TERAS
7	7513232.562	4691398.813	616.454	PERDHESA-TERAS
8	7513230.254	4691402.965	616.454	PERDHESA-TERAS
15	7513240.898	4691397.155	616.227	PUSET-FEKAL
3	7513232.952	4691397.414	617.039	SHKALET
4	7513232.404	4691397.145	616.933	SHKALET
5	7513232.259	4691398.658	616.931	SHKALET
19	7513241.025	4691398.981	616.645	SHTYLL-ELEKTRIKE
268	7513216.930	4691395.995	616.444	Shufer
51	7513207.233	4691445.773	617.131	ST1
52	7513257.218	4691379.223	616.137	ST2
53	7513233.834	4691417.520	616.607	ST3
33	7513233.815	4691393.063	622.419	STREHA
34	7513231.765	4691396.770	622.364	STREHA
35	7513231.463	4691396.611	622.415	STREHA
36	7513230.182	4691398.874	622.538	STREHA
37	7513229.829	4691398.682	622.760	STREHA
38	7513227.902	4691402.081	622.493	STREHA
39	7513217.515	4691396.266	623.616	STREHA
41	7513222.772	4691386.881	623.616	STREHA

Nr	Y	X	H	DSC
54	7513235	4691417	616.613	FS1
20	7513227	4691402	623.616	KULMI
16	7513233	4691404	616.465	KYQJE-UJSJELLES
17	7513235	4691406	616.583	MURI
18	7513243	4691396	616.444	MURI
267	7513223	4691385	616.444	MURI
42	7513205	4691403	616.454	OBJEKT-FQINJ
43	7513206	4691403	616.454	OBJEKT-FQINJ
44	7513208	4691400	616.454	OBJEKT-FQINJ
45	7513197	4691398	616.454	OBJEKT-FQINJ
46	7513210	4691395	616.454	OBJEKT-FQINJ
47	7513210	4691395	616.454	OBJEKT-FQINJ
48	7513211	4691394	616.454	OBJEKT-FQINJ
49	7513211	4691393	616.454	OBJEKT-FQINJ
50	7513211	4691392	616.454	OBJEKT-FQINJ
303	7513202	4691387	616.454	OBJEKT-FQINJ
9	7513228	4691401	616.454	PERDHESA
10	7513230	4691397	616.454	PERDHESA
11	7513231	4691396	616.454	PERDHESA
12	7513231	4691397	616.454	PERDHESA
13	7513233	4691393	616.454	PERDHESA
14	7513218	4691396	616.454	PERDHESA

Shpjegues:

- Kufiri kadastral (nga SIKTK-G)
- Ndërtesa në trajtim për legalizim
- Ndërtesa tjera
- Terasa
- Shtyllë elektrike
- Pusetë e ujësjellësit
- Pusetë e ujërave të zeza
- Strehët
- Shkallët
- 91 Pikë e objekteve fqinje
- Rr. Emri i rrugës
- P4 Pikë e rrjetës gjeodezike
- 131 Pikë e strehëve
- 81 Pikë e terasës
- 10 Pikë e objektit
- 93 Pikë e murit
- 92 Pikë e kulmit

Rilevoi / Snimi: SEAD PRUSHI

(emri dhe mbiemri i gjedetit/kompanisë/ ime i prezime gedeta/ kompanije)

Nr. i licencës / Br. licence: 152

Data e rilevimit / Datum snimanja: 01.09.2020

Nënshkrimi / Potpis: _____

V.V.